


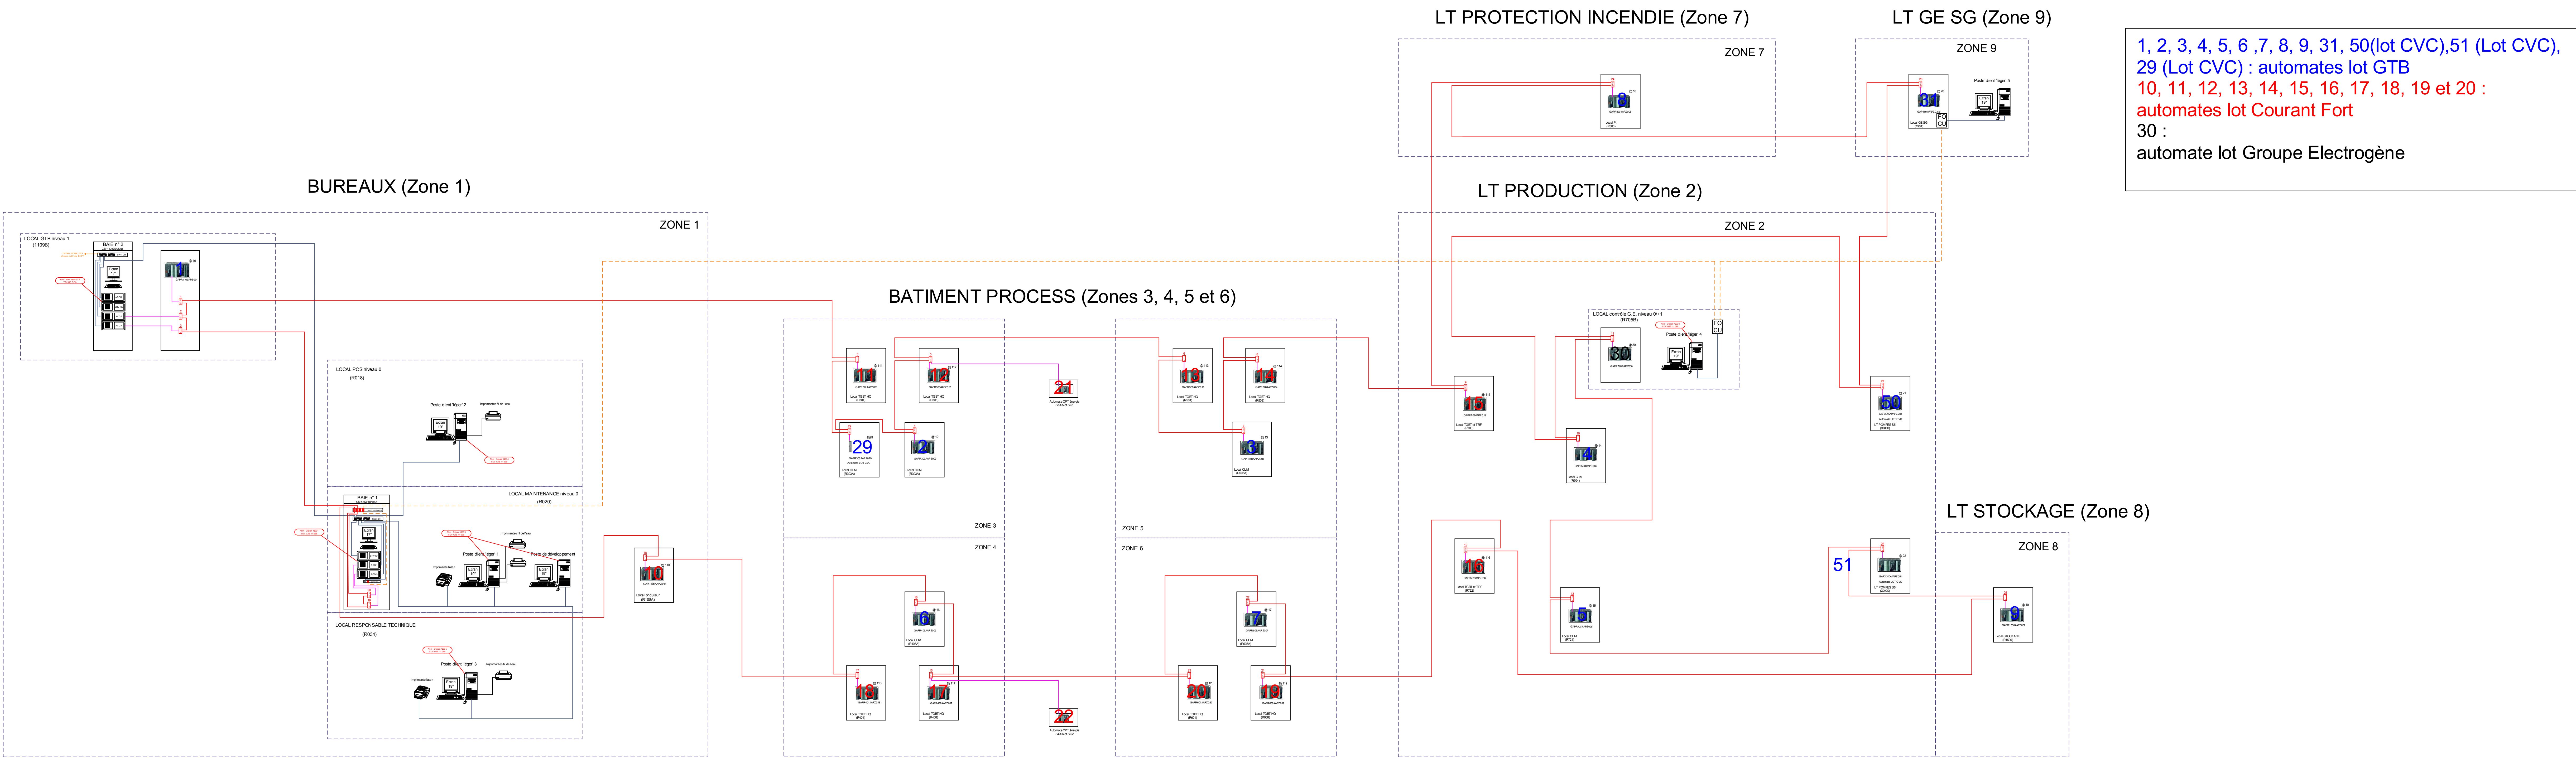



1, 2, 3, 4, 5, 6, 7, 8, 9, 31, 50 (lot CVC), 51 (Lot CVC),
29 (Lot CVC) : automates lot GTB
10, 11, 12, 13, 14, 15, 16, 17, 18, 19 et 20 :
automates lot Courant Fort
30 :
automate lot Groupe Electrogène

LEGENDE

- Automate S7-400 'SIEMENS'
- Automate 1500H 'SIEMENS'
- Module d'entrées/sorties déportés ET200S 'SIEMENS'
- Module d'entrées/sorties déportés ET200SP 'SIEMENS'
- Automate CC6400 'CARRIER'
- Passerelle RAMSES CCN/MODBUS 'CARRIER'
- Switch SIEMENS SCALANCE XC206-2
- Switch Phoenix contact FL SFN 16TX
- Carte d'interface MODBUS 'SIEMENS'
- Module externe communiquant en MODBUS ('CPT' : module de mesures électriques type DIRIS)
- Module interface optique/cuivre
- Interface IP
- Tableaux électriques lot CFO
- Module Transfert De Charge
- Armoires de climatisation
- Centrale traitement d'air
- Passerelles de communication 'HIROSS'
- API WAGO (Passerelle de com. MODBUS IP / MODBUS RS)
- WESTERMO EDW100 (Passerelle de com. MODBUS IP / MODBUS RS)
- A titre d'information, non remonté à la GTB

Types de liaison

- Liaisons type 'filaire'
- Liaisons type MODBUS
- Liaisons type 'PROFIBUS' cuivre
- Liaisons type 'PROFIBUS' fibre optique
- Liaisons type 'réseau propriétaire HIROSS'
- Liaisons type 'réseau propriétaire CARRIER - CCN -'
- Liaisons type 'ETHERNET' cuivre
- Liaisons type 'ETHERNET' fibre optique
- Liaisons type 'MODBUS IP' cuivre
- Liaisons type 'BACnet IP' cuivre
- Liaisons type 'PROFINET IP' cuivre

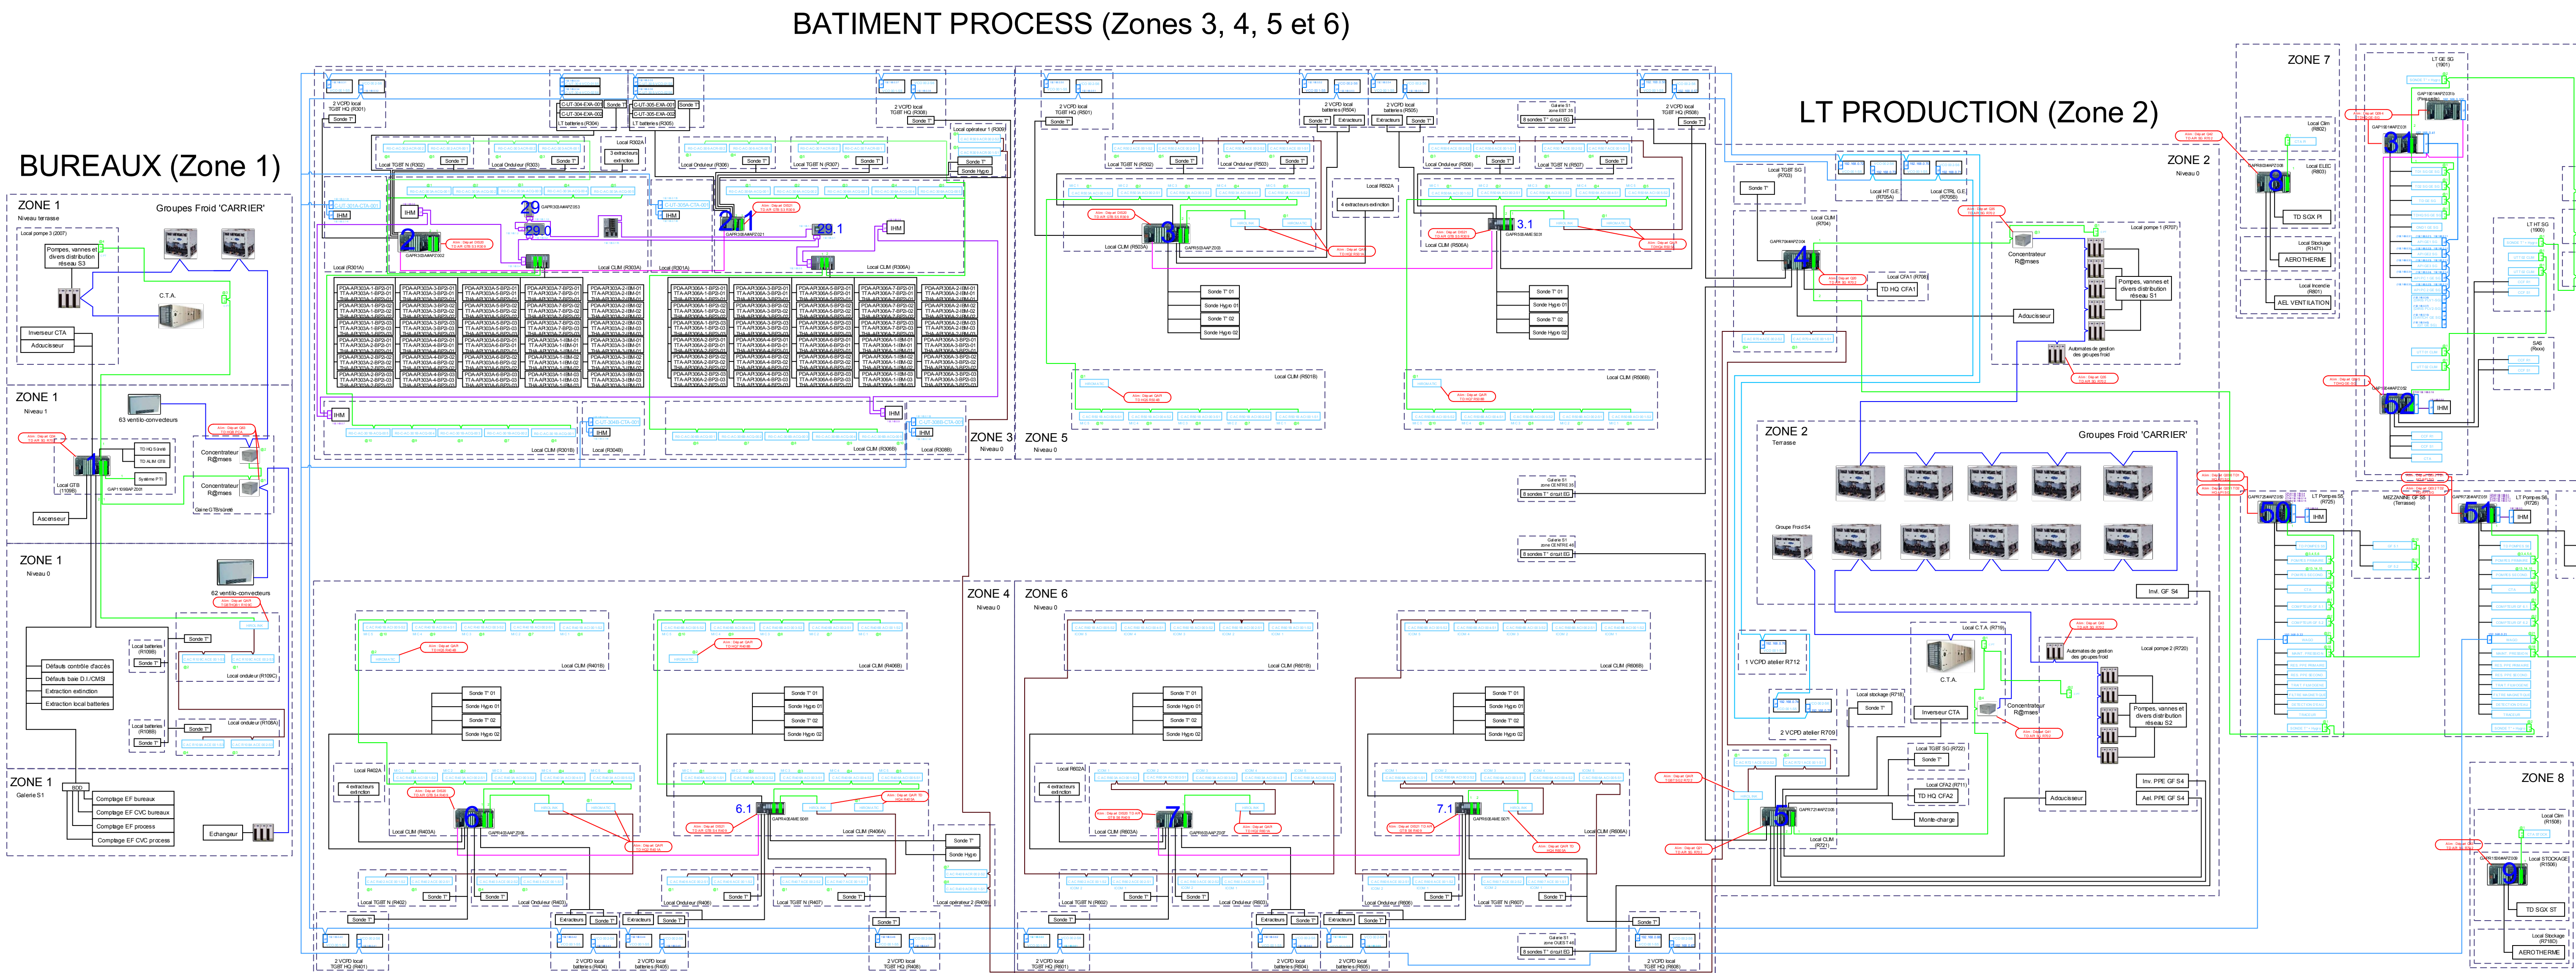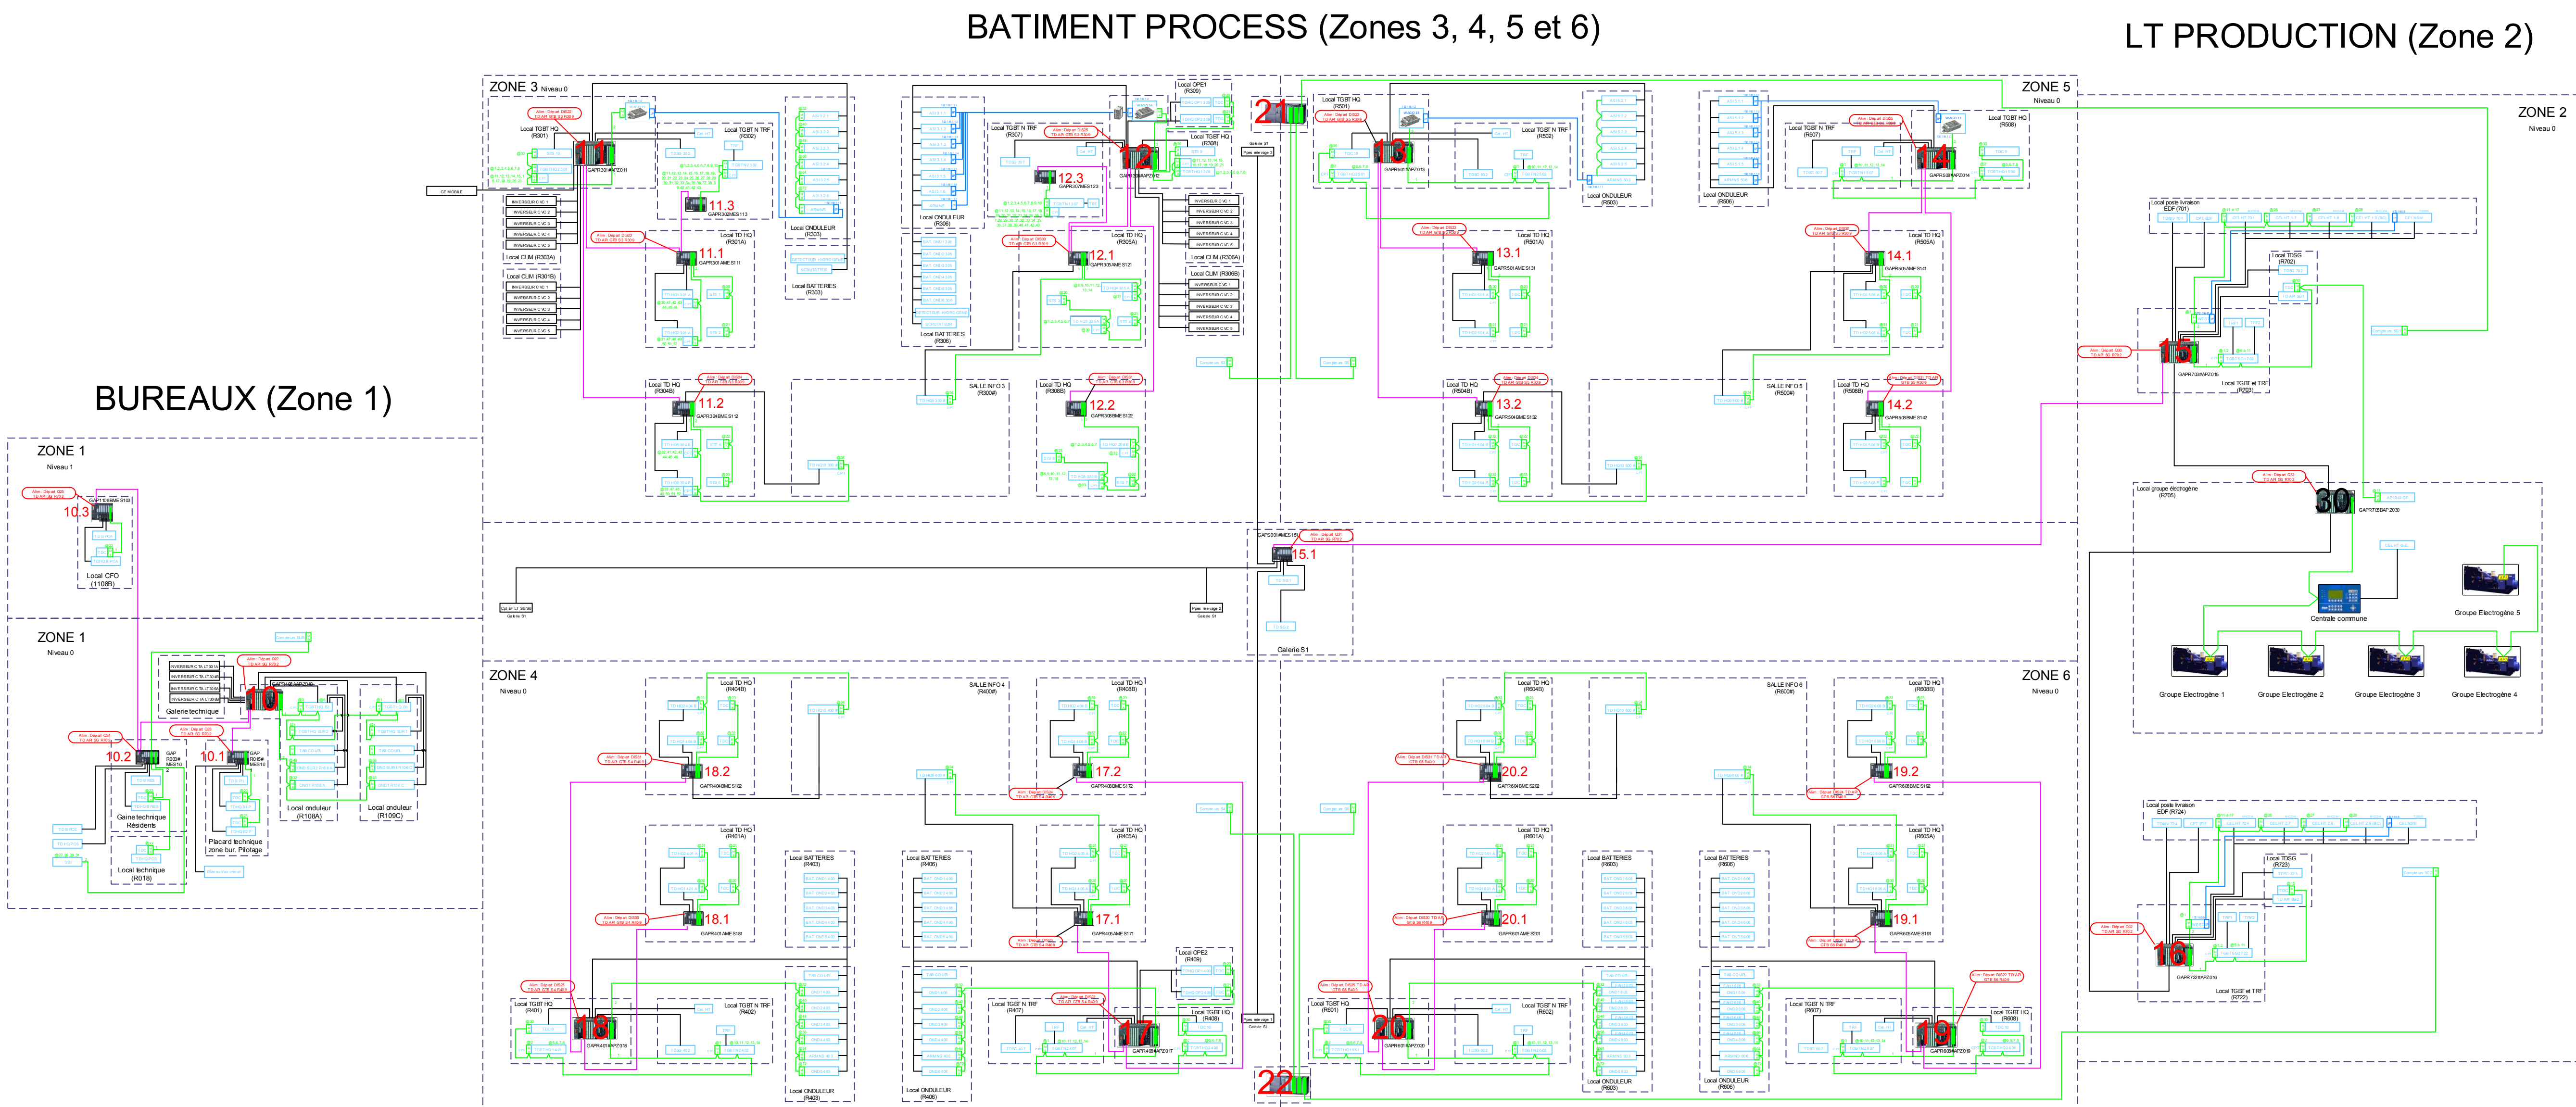

Centre de Traitement Informatique MARNE NORD

Parc d'activités Gustave Eiffel
ZAC de BUSSY SUD
Avenue Gutenberg
77600 - BUSSY-SAINT-GEORGES

Maitre d'ouvrage SNP - PARISAS 177 RUE DE LA REPUBLIQUE 93000 PARIS Tel : 01 41 41 41 41 Fax : 01 41 41 41 41	Exploitant BP 3 BIP PARISAS FOR INNOVATION 14 rue de la République 93000 PARIS Tel : 01 41 41 41 41 Fax : 01 41 41 41 41
Bureau de contrôle ARTELIA 14 rue de la République 93000 PARIS Tel : 01 41 41 41 41 Fax : 01 41 41 41 41	Sécurité Protection Santé ARTELIA 14 rue de la République 93000 PARIS Tel : 01 41 41 41 41 Fax : 01 41 41 41 41
Maitre d'œuvre ARTELIA 14 rue de la République 93000 PARIS Tel : 01 41 41 41 41 Fax : 01 41 41 41 41	SW APILOG Automation 3 rue Galvani 91302 MASSY

SYNOPTIQUE GENERAL
ARCHITECTURE G.T.B.

DATE	14/12/05
DATE MODIF	09/12/19
REVISION	006
DATE	14/12/05
DATE MODIF	09/12/19
REVISION	006